


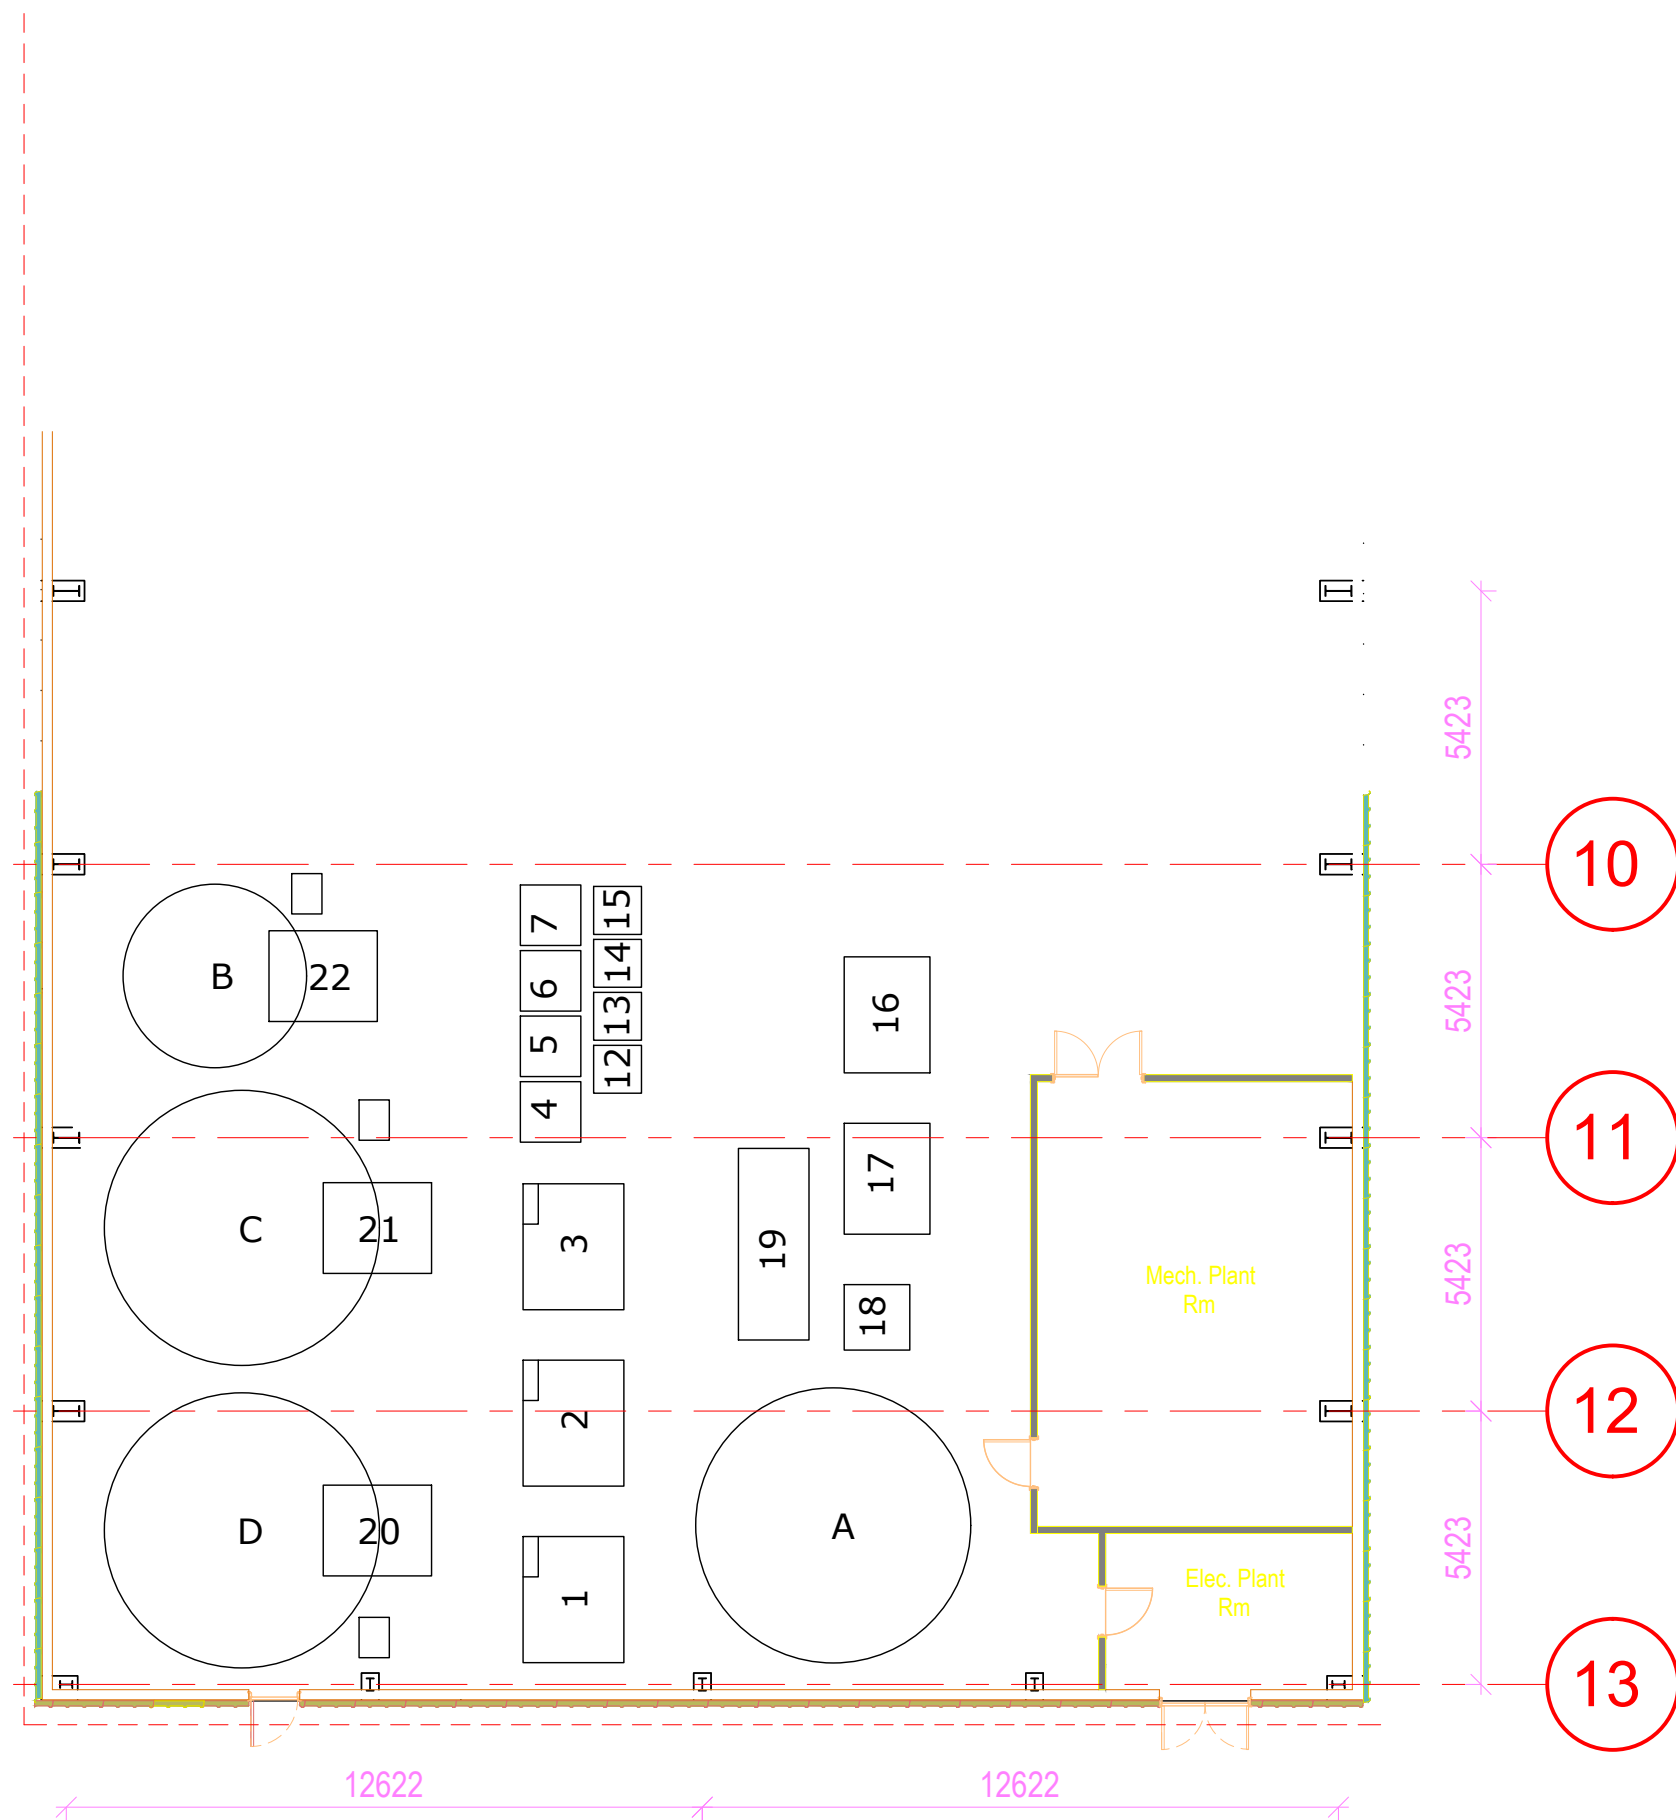

- 1 Fertilizer unit 1 2500x2000
- 2 Fertilizer unit 2 2500x2000
- 3 Fertilizer unit Nursery + Hydrofor 2500x2000
- 4 A11 Fertilizer container 1200x1200
- 5 B11 Fertilizer container 1200x1200
- 6 A12 Fertilizer container 1200x1200
- 7 B12 Fertilizer container 1200x1200
- ~~8 A21 Fertilizer container 1200x1200~~
- ~~9 B21 Fertilizer container 1200x1200~~
- ~~10 A22 Fertilizer container 1200x1200~~
- ~~11 B22 Fertilizer container 1200x1200~~
- 12 Nursery A1 Fertilizer container 950x950
- 13 Nursery B1 Fertilizer container 950x950
- 14 Nursery A2 Fertilizer container 950x950
- 15 Nursery B2 Fertilizer container 950x950
- 16 Hydrofor pump Reverse osmose 1700x2300
- 17 Reverse osmose water softner 2200x1700
- 18 Reverse osmose GAC 1300x1300
- 19 Reverse osmose 3800x1400
- 20 Drain pit 1 5000L + cloth filter + container
- 21 Drain pit 2 5000L + cloth filter + container
- 22 Drain pit Nursery 5000L + cloth filter + container
- A Freshwater silo
- B Drain water nursery + oxygen
- C Drain water dep1 + oxygen
- D Drain water dep 2 + pxygen

|     |           |                                                                                |          |        |
|-----|-----------|--------------------------------------------------------------------------------|----------|--------|
| D   |           |                                                                                |          |        |
| C   |           |                                                                                |          |        |
| B   |           |                                                                                |          |        |
| A   | 8-3-2021  | Changed layout, cloth filter above silo, reduced number of AB fert. containers | RH       |        |
| NR. | Datum dd. | Omschrijving van de wijziging                                                  | Getekend | Gezien |

Layout Water Technical Room

|               |  |              |               |         |           |
|---------------|--|--------------|---------------|---------|-----------|
| Fischer Farms |  | Status       |               | Concept |           |
| ----          |  | Projectnr.   |               | ----    |           |
| GB            |  | Gezien       |               | Datum   |           |
|               |  | Tekenaar     | R. Hogervorst | Datum   | 08-Mar-21 |
|               |  | Formaat      | A3            | Schaal  | -         |
|               |  | Tekening nr. |               | Blad    |           |
|               |  | 200          |               | 01      |           |