


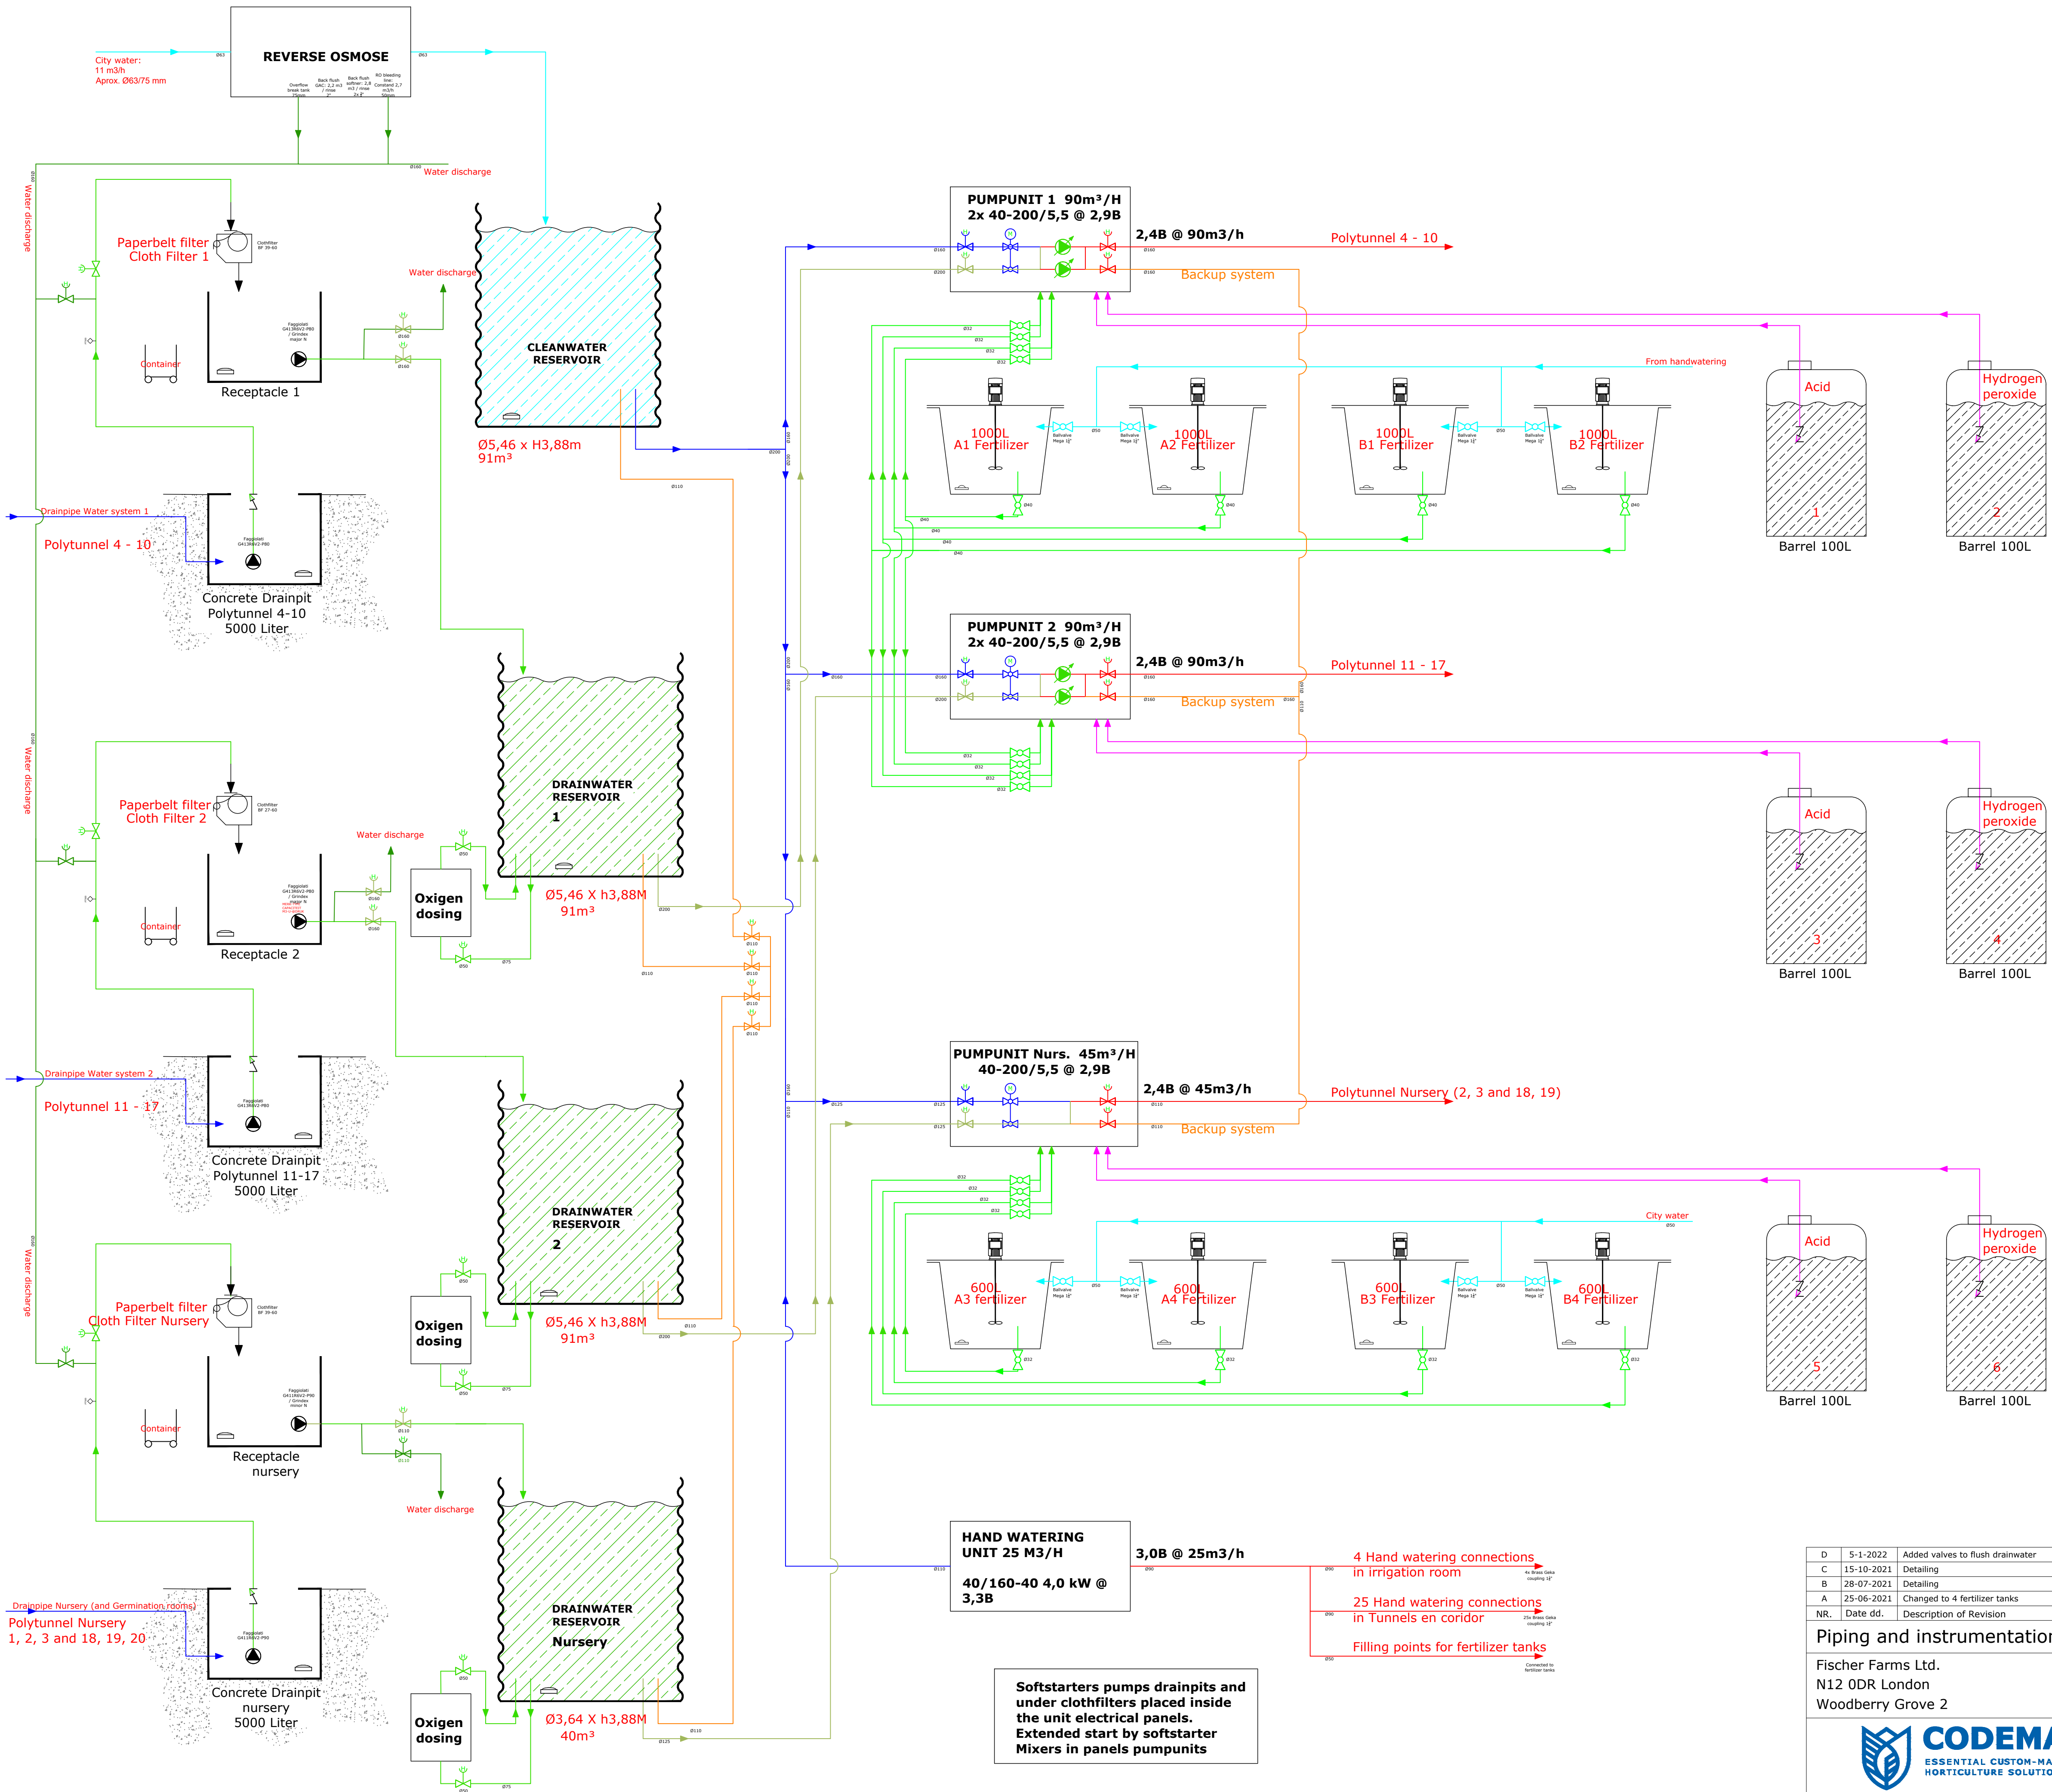

D	5-1-2022	Added valves to flush drainwater	RH	
C	15-10-2021	Detailing		
B	28-07-2021	Detailing	RH	
A	25-06-2021	Changed to 4 fertilizer tanks	RH	
NR.	Date dd.	Description of Revision	Drawn by	Checked
Piping and instrumentation diagram				
Fischer Farms Ltd. N12 0DR London Woodberry Grove 2			Status	Concept
			Projectno.	S021101551 / 3210630
			Checked	Date
			Drawn by	Date 08-Apr-21
			Size A1	Scale
			Drawingno.	Sheet
			100	01

This drawing is property of the company belonging to Codema Systems Group BV. No rights can be derived from this drawing. For the use of information or sharing of information with third parties, written consent must first be granted. In all cases where we are the contractor, this document is subject to the General Terms of Sale and Delivery Codema Systems Group. In all cases where we are the client, the General Purchase Conditions Codema Systems Group apply to this document. This document and the information contained herein is property of the company belonging to Codema Systems Group BV and it is not permitted, among other things, to copy, disclose or use, in the broadest sense of the word, the drawing or the information contained therein without written consent.